

Фасад в осях В-А

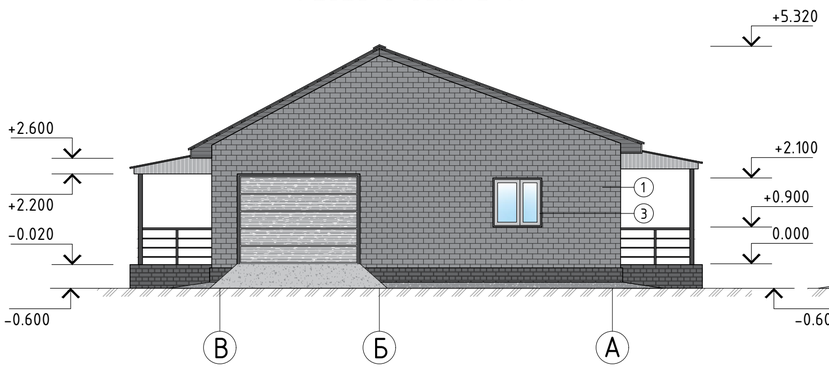


Фасад в осях 1-3

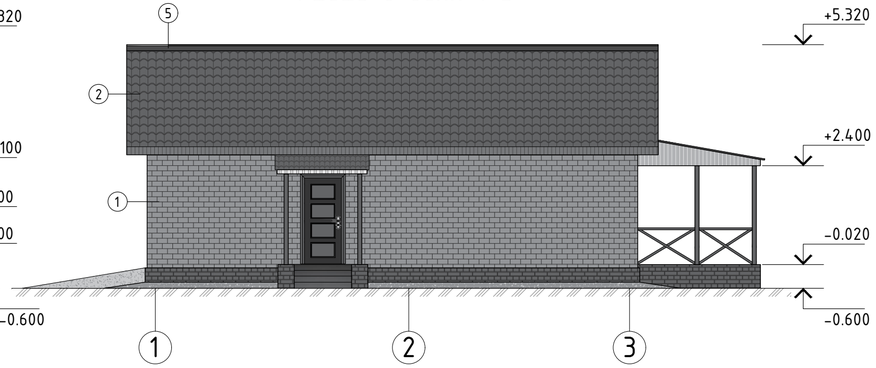


Ведомость отделки фасадов

Поз. отделки	Наименование элемента фасада	Наименование материала отделки	Наименование и номер эталона цвета или образец колера
1	Стены	Металлосайдинг	RAL 7031 (Стально-серый)
2	Кровля	Металлочерепица	RAL 7024 (Мокрый асфальт)
3	Окна	ПВХ	RAL 9003 (Сигнально-белый)
4	Дверь	Металлическая	RAL 7016 (Антрацитово-серый)
5	Фасонные элементы	Металлические	RAL 7024 (Графитовый серый)
6	Крыльцо	Керамогранитные плиты	RAL 7037 (Пыльно-серый)

Фасад в осях А-В

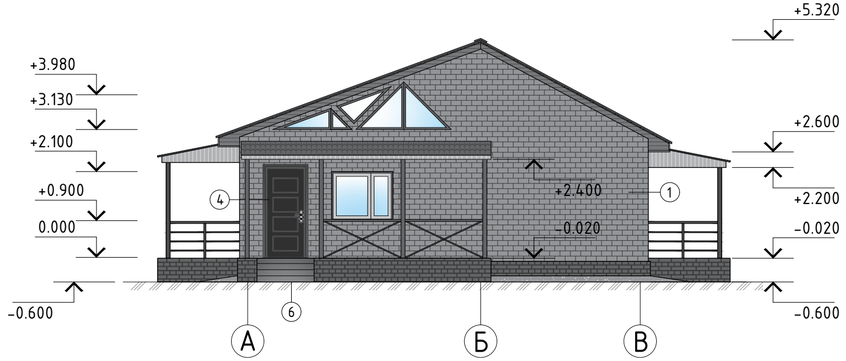

Фасад в осях 3-1

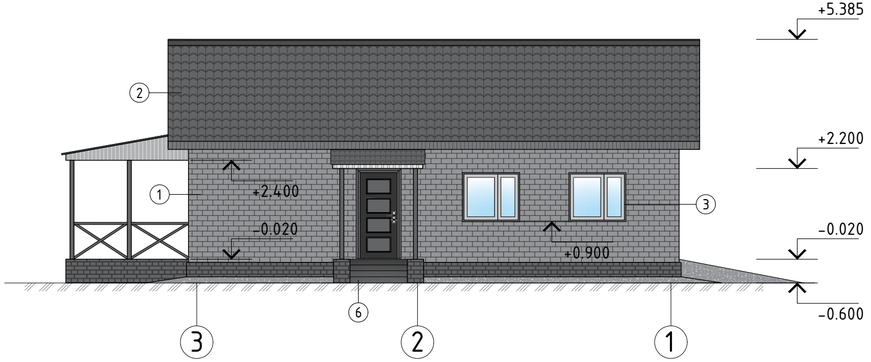

Согласовано

Взам. инв. №


Подпись и дата

Инв. № подл.

Изм.	Кол. уч.	Лист	№ док.	Подп.	Дата	Заказ №: АКК-98/06-26РИ-АС			
						Строительство индивидуального жилого дома и переоборудование существующего жилого дома под баню по адресу: СКО, г. Петропавловск, ул. Ынтымақ д.12			
ГИП		Обыденный А.Н.			08.26	Индивидуальный жилой дом	Стадия	Лист	Листов
Разработал		Кособоков В.А.			08.26		ЭП	3	
Проверил		Обыденный А.Н.			08.26				
Н.контр.		Обыденный А.Н.			08.26	Фасад в осях В-А; Фасад в осях А-В; Фасад в осях 1-3; Фасад в осях 1-3;	ТОО "Альтернатива" Лицензия №17018764 г.Петропавловск		

Формат А3х1.5

План на отметке 0.000

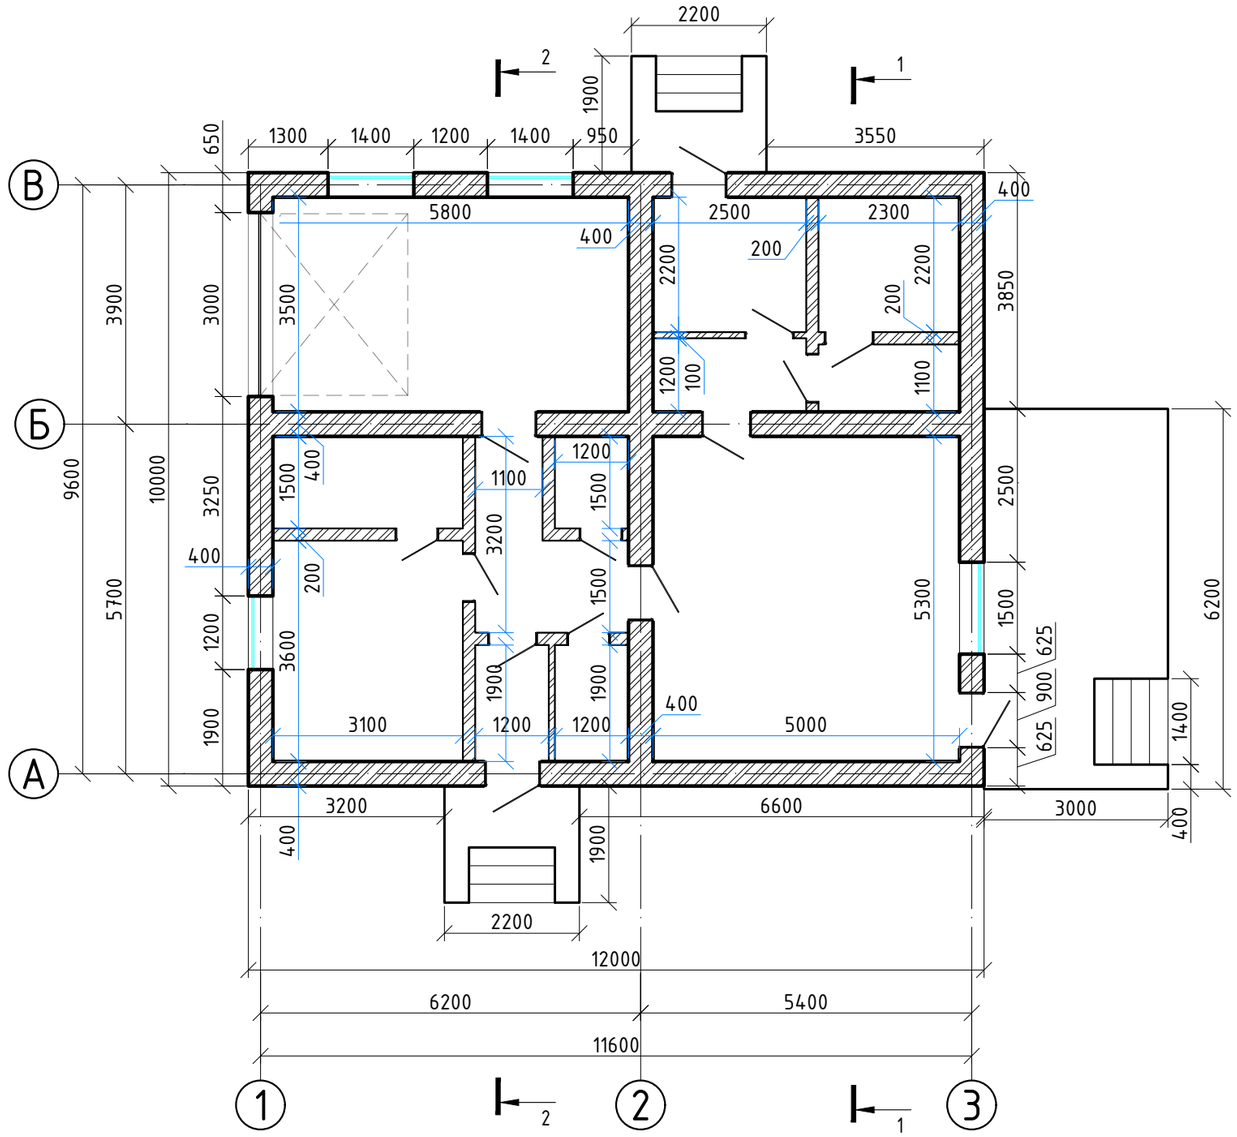

Экспликация помещений

Номер поме-щения	Наименование	Площадь, м²	Кат. поме щения
1	Тамбур	1,80	
2	Прихожая	8,62	
3	Гараж	20,30	
4	Санузел	1,80	
5	Спальня	11,16	
6	Гардеробная	4,75	
7	Кухня-гостинная	26,49	
8	Кладовая	2,20	
9	Постирочная	1,92	
10	Коридор	2,20	
11	Сауна	4,40	
12	Котельная	5,20	
	ИТОГО:	90.84	

Согласовано

Взам. инв. №

Подпись и дата

Инв. № подл.

Изм.	Кол. уч.	Лист	№ док.	Подп.	Дата
ГИП		Обыденный А.Н.			08.26
Разработал		Кособоков В.А.			08.26
Проверил		Обыденный А.Н.			08.26
Н.контр.		Обыденный А.Н.			08.26

Заказ №: АКК-98/06-26РИ-АС

Строительство индивидуального жилого дома и переоборудование существующего жилого дома под баню по адресу: СКО, г. Петропавловск, ул. Ынтымақ д.12


Индивидуальный жилой дом

Стадия	Лист	Листов
ЭП	4	


План на отметке 0.000

ТОО "Альтернатива"
Лицензия №17018764
г.Петропавловск


Разрез 1-1

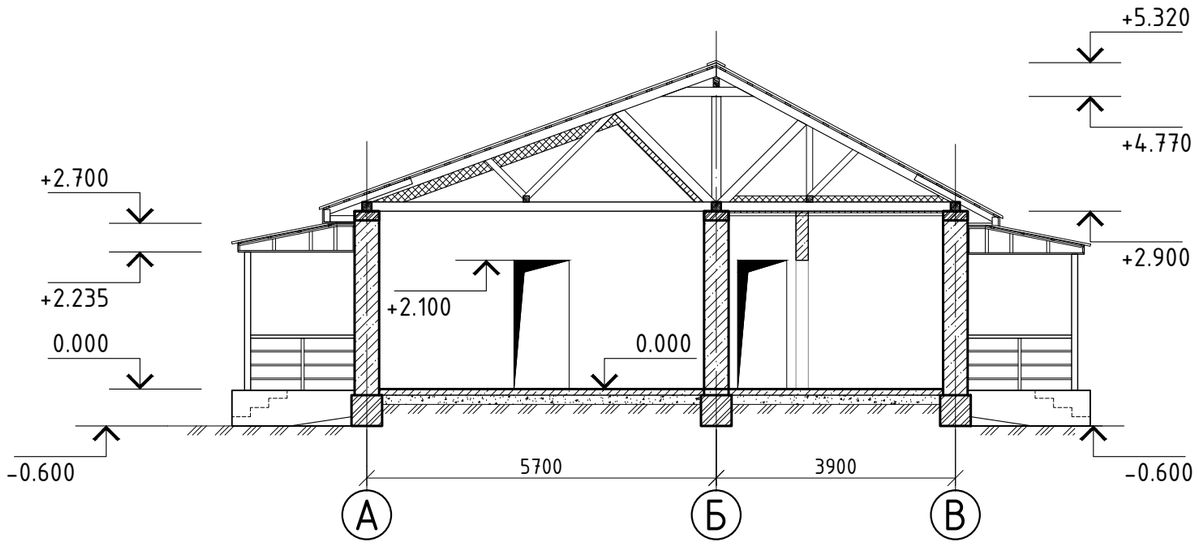

Разрез 2-2

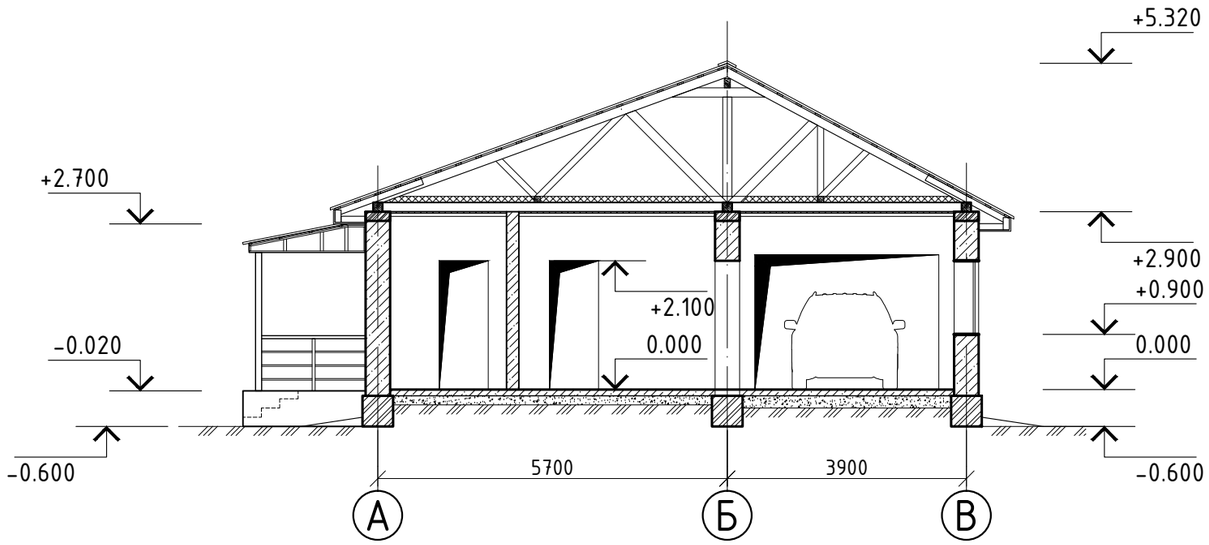

План кровли

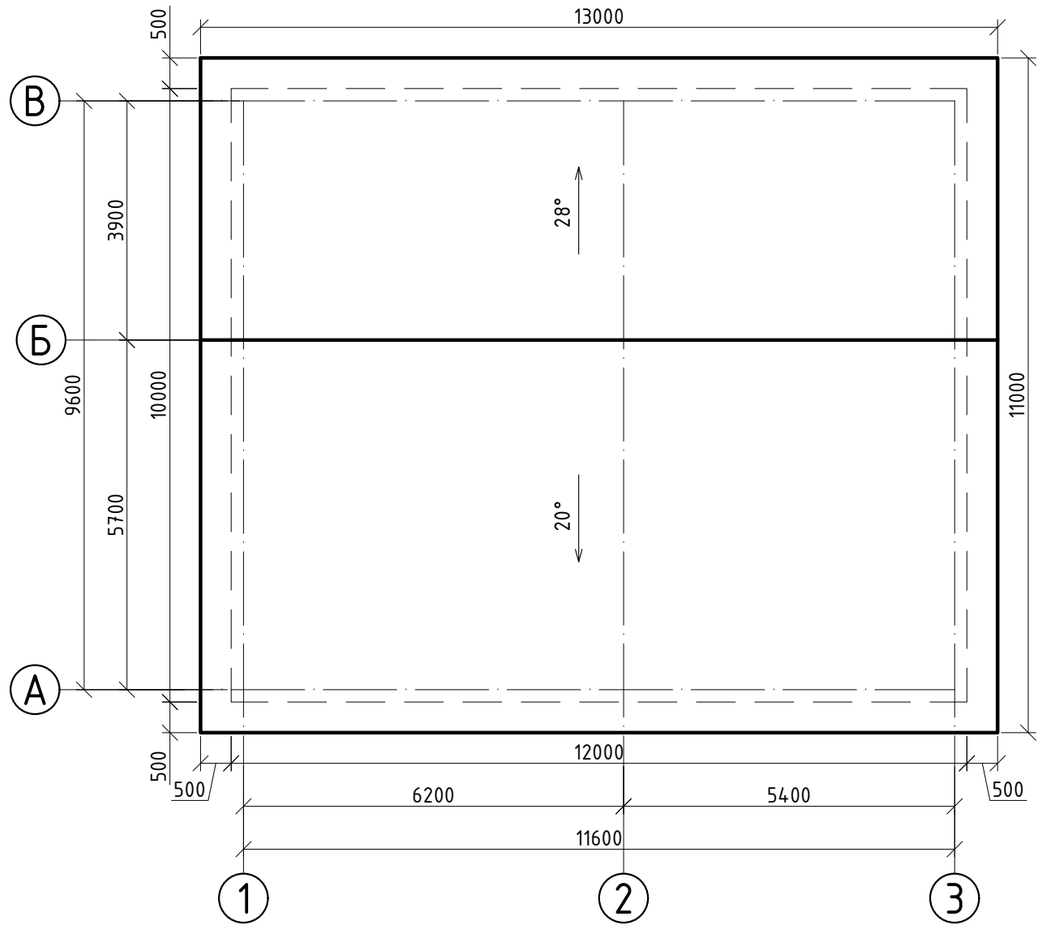

Согласовано

Взам. инв. №

Подпись и дата

Инв. № подл.

Изм.	Кол. уч.	Лист	№ док.	Подп.	Дата	Заказ №: АКК-98/06-26РИ-АС		
						Строительство индивидуального жилого дома и переоборудование существующего жилого дома под баню по адресу: СКО, г. Петропавловск, ул. Ынтымақ д.12		
ГИП		Обыденный А.Н.			08.26	Индивидуальный жилой дом	Стадия: ЭП	Лист: 5	Листов:
Разработал		Кособоков В.А.			08.26				
Проверил		Обыденный А.Н.			08.26				
Н.контр.		Обыденный А.Н.			08.26	Разрез 1-1; Разрез 2-2; План кровли	ТОО "Альтернатива" Лицензия №17018764 г.Петропавловск		